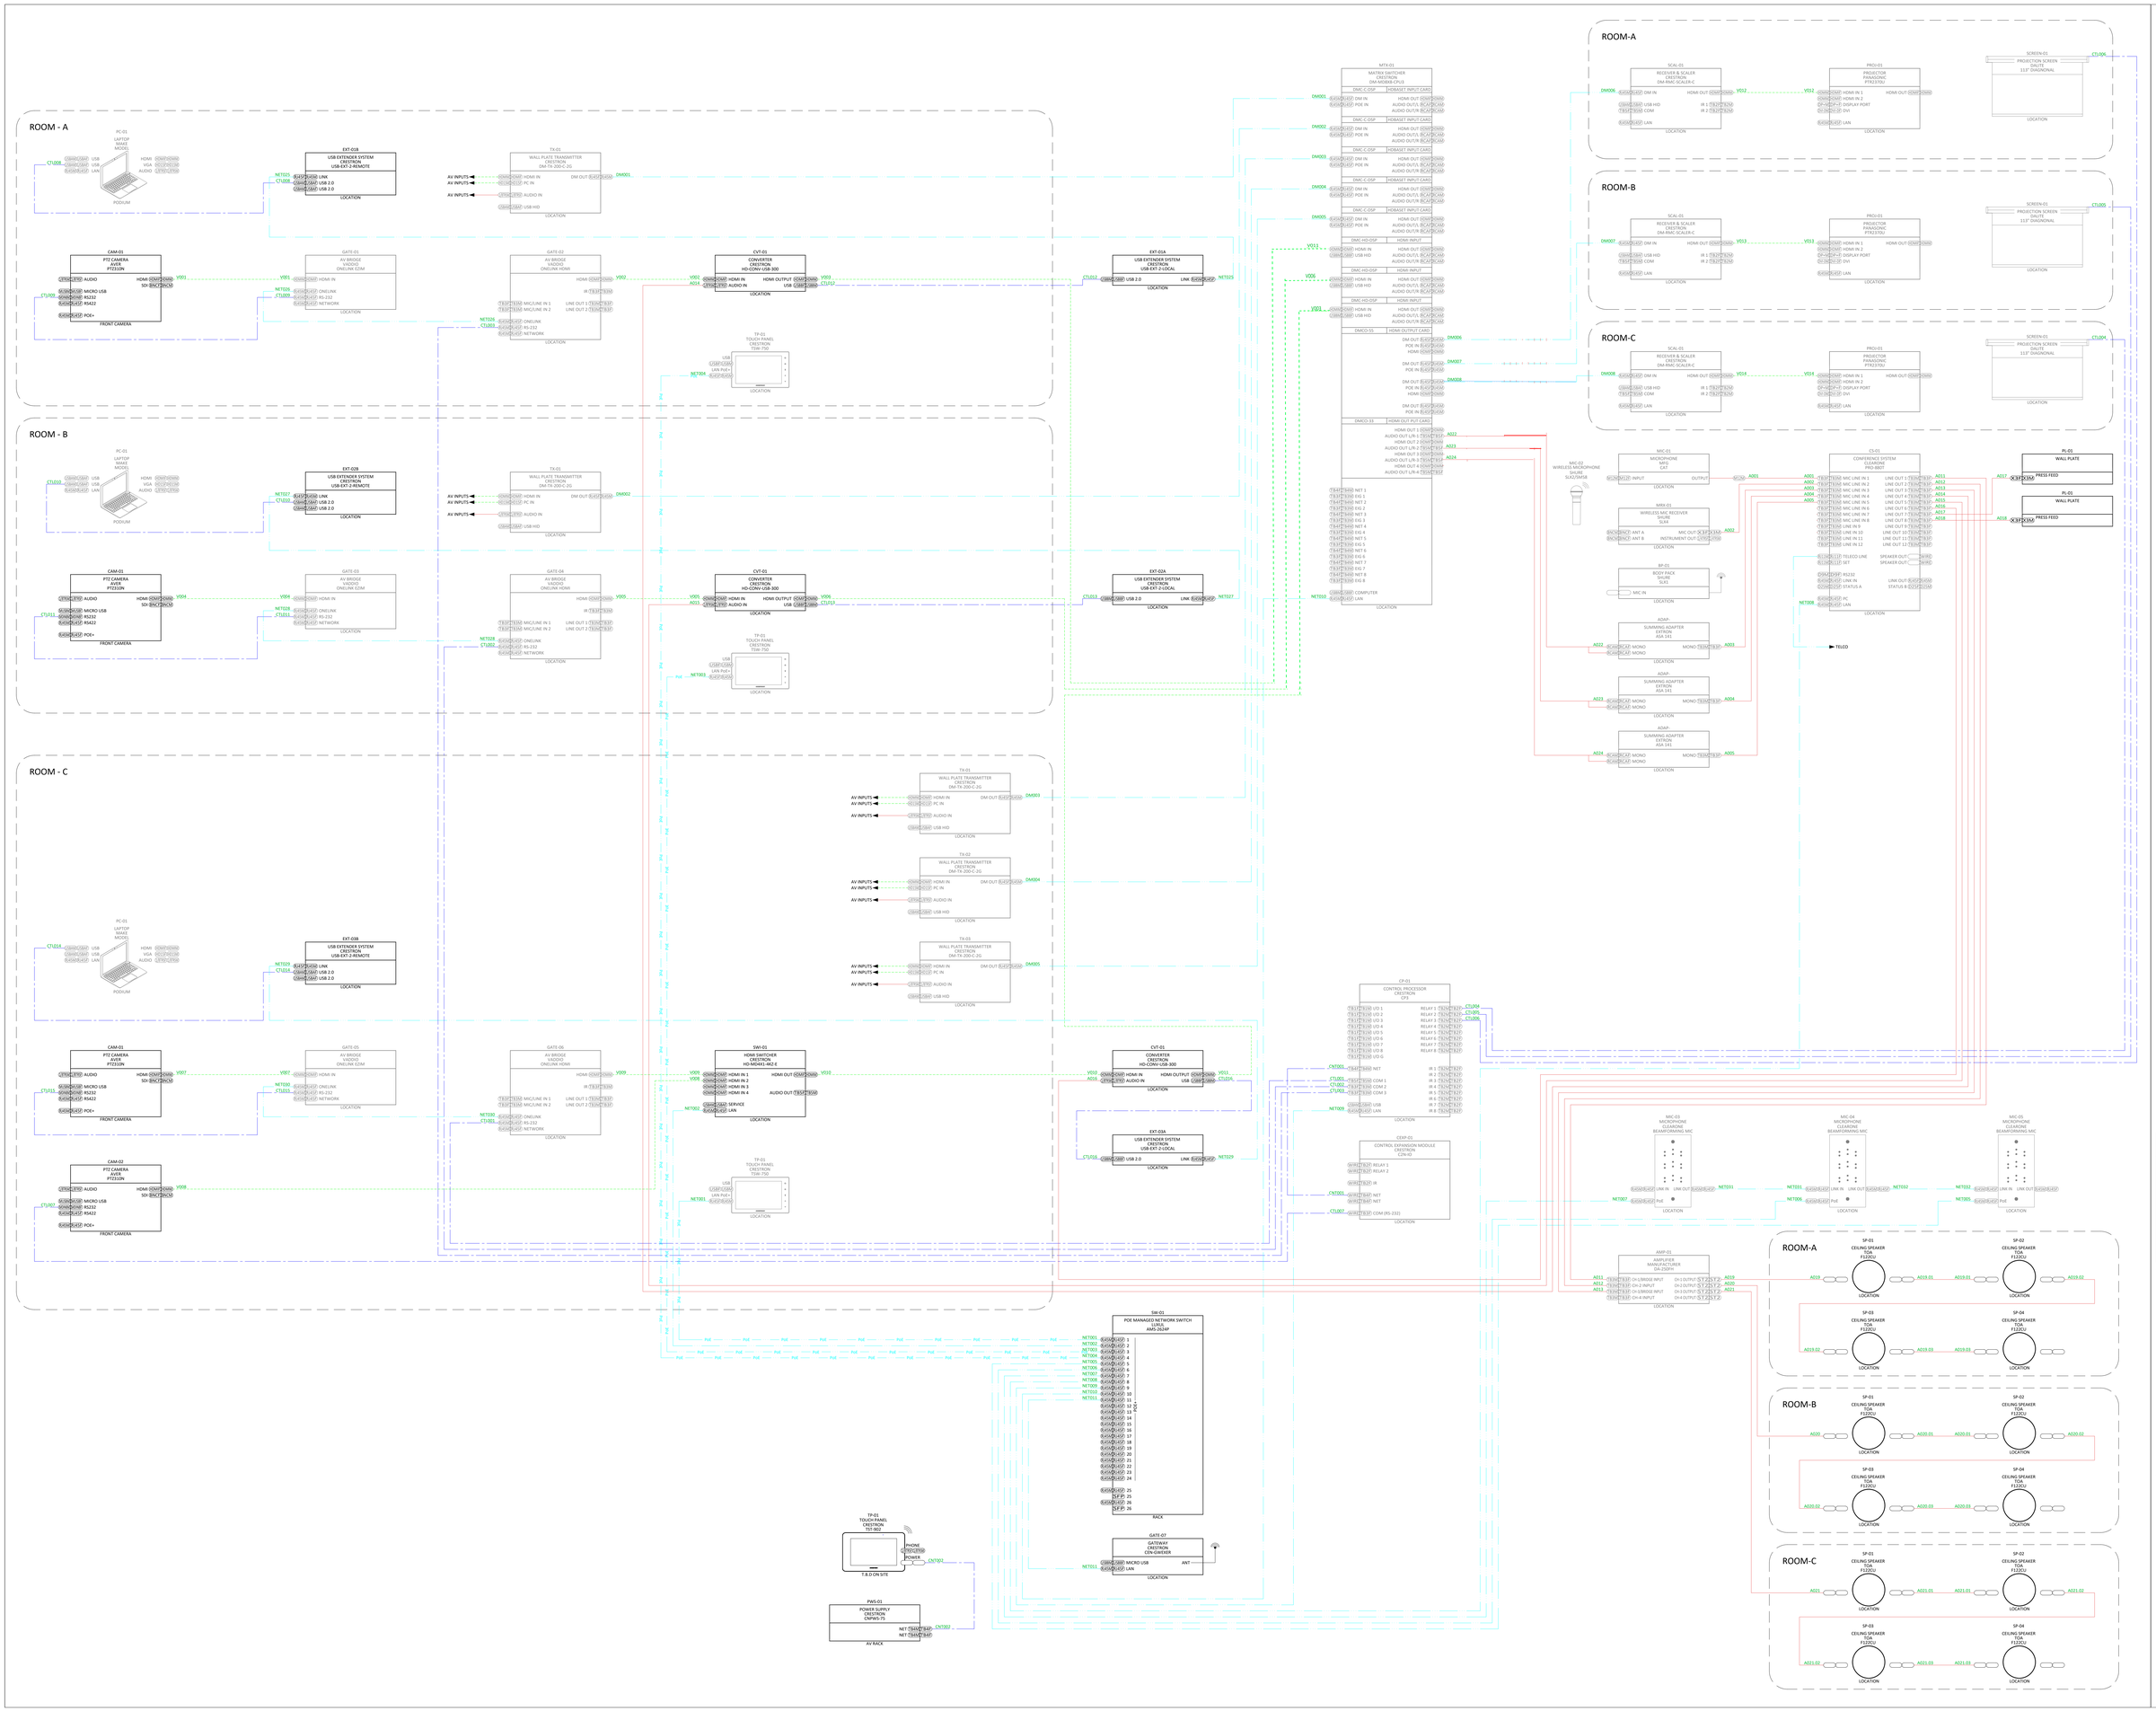

By using this document, the user accepts the following terms and conditions:

This document shall be used for its intended and approved purpose only.

All information herein represented are conceptual and are intended as general reference only. No reliance should be placed on such information. Although Solotech Inc. believes that all information herein represented is accurate, Solotech Inc. makes no assurance that such information will prove to be correct.

All information herein represented must be verified and approved by mechanical, structural engineers and contractors. Users are cautioned to perform their own investigation and analysis.

Any user of the information herein represented agrees that it assumes all liability arising from such use. Solotech Inc. makes no representations or warranties, express or implied, as to the accuracy or adequacy of, the use or misuse of the information available in this document.

Solotech Inc. reserves the right to modify, revise or change this document in its sole and absolute discretion, without notice.

All information herein represented is subject to all national codes and regulations.

This document contains copyrighted and confidential information. Any unauthorized reproduction, in whole or in part, without the prior written consent of Solotech Inc. The type of loudspeaker enclosures and their relative or absolute position is the property of Solotech Inc.

CABLE LEGEND

- AUDIO
- AVC CAT6/8 SHIELDED CAT.x
- CONTROL
- DMX
- FIBER
- NET
- NET PoE
- POWER
- VIDEO
- RF
- TBD
- BY OTHERS

STANDARD CABLE NUMBERS
A: AUDIO
CTL: CONTROL
CNT: CRESNET
DMNT: CRESTRON DMNET
DMX: DMX
DTP: EXTRON DTP
F: FIBER
HDBT : HDBaseT
NET : NETWORK
PW: ELECTRICITY
RF : RADIO FREQUENCY
SP: SPEAKER
V: VIDEO
AVC: AUDIO/VIDEO OVER CAT5/6

EXAMPLE:
CNT001
- SEQUENTIAL CODE
- SIGNAL TYPE

123456-XXX
- DRAWING NUMBER
- PROJECT NUMBER

NO	DATE	BY	DESCRIPTION
00	2023/09/12	SP	FOR INSTALLATION

CLIENT
HEALTH SCIENCES NORTH

SOLOTECH simply spectacular

PROJECT
AV SOLUTION AT HEALTH SCIENCES NORTH

ADDRESS
41 RAMSEY LAKE ROAD
SUDBURY ONTARIO
P3E 5J1 CANADA

PROJECT #
PJCA005200

REPRESENTATIVE
J.CHISHOLM

PROJECT MANAGER
V.COGGINS

TITLE
SINGLE LINE DIAGRAM
LECTURE ROOM

DRAWN BY: S.PAUL
APPROVED BY: PRABA.K
DATE CREATED: 2023/09/18
DATE LAST SAVED: 2023/09/25
SCALE: N.T.S.
SHEET SIZE: ARCH E
FILE NAME: PJCA005200 - 200 SCHEMA.dwg
DRAWING NAME: PJCA005200-205

DATE PRINTED: 9/25/2023

C:\USERS\SAFA.PAUL\SOLOTECH CORVUS\ - AV SOLUTIONS AT HEALTH SCIENCES NORTH_\PJCA005200\06_DRAWINGS